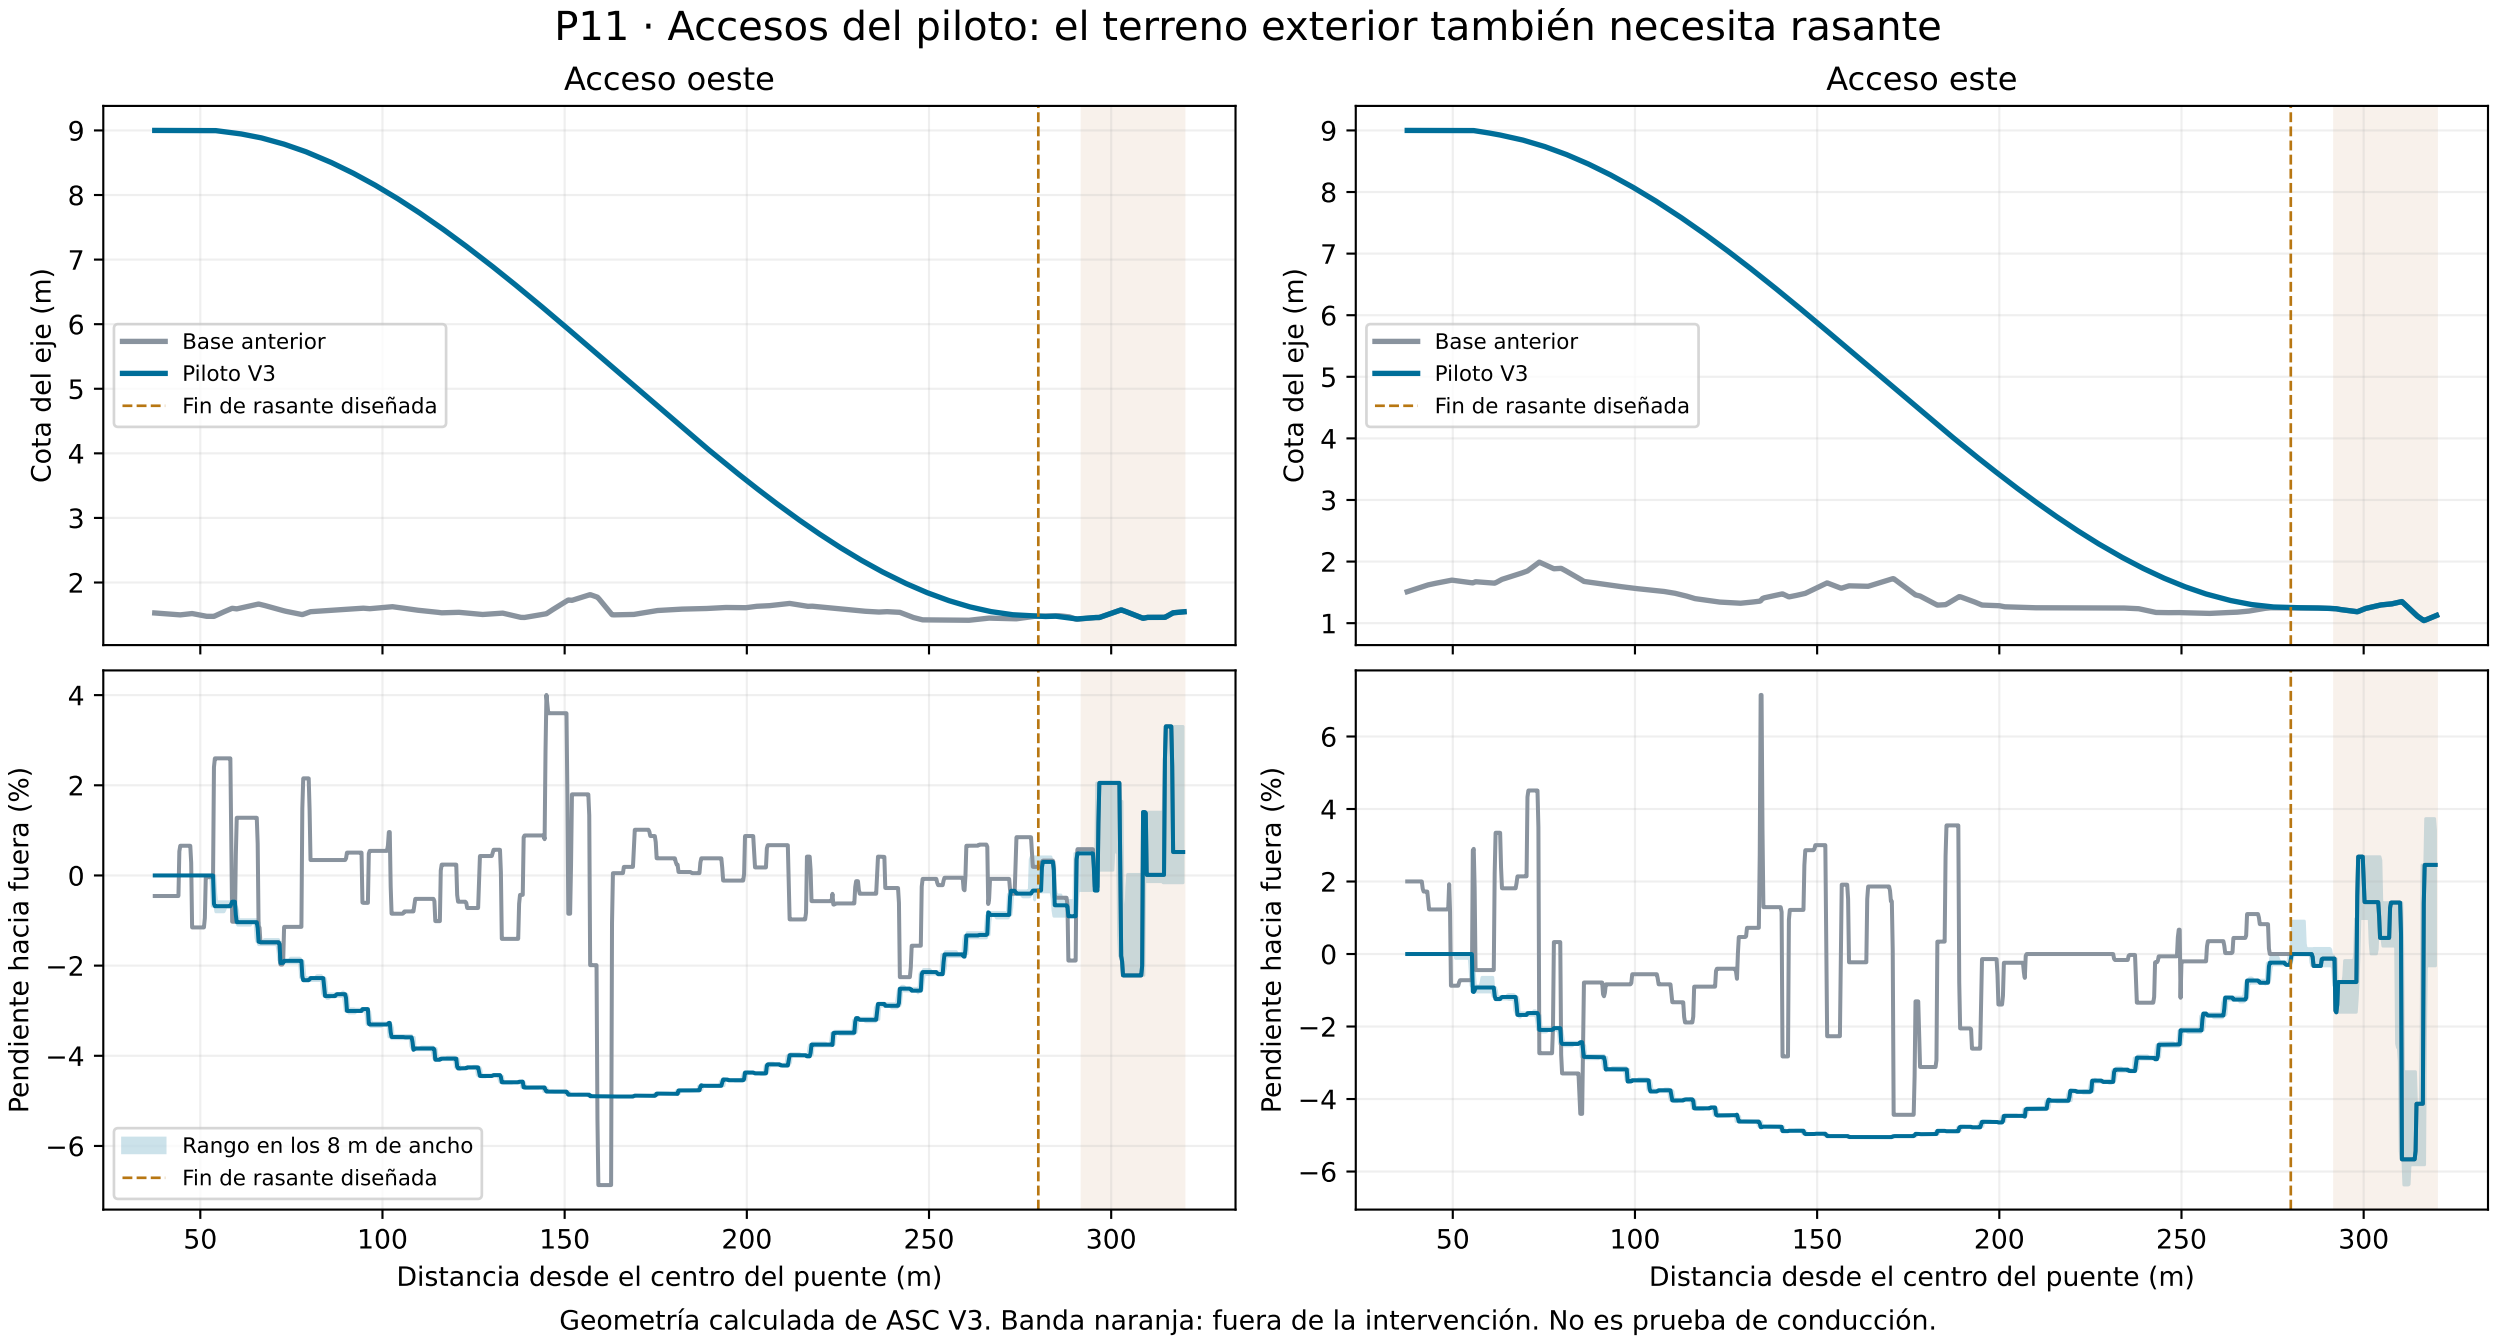

P11 · Accesos del piloto: el terreno exterior también necesita rasante
Acceso oeste
Acceso este
Cota del eje (m)
Base anterior
Piloto V3
Fin de rasante diseñada
Pendiente hacia fuera (%)
Rango en los 8 m de ancho
Distancia desde el centro del puente (m)
Geometría calculada de ASC V3. Banda naranja: fuera de la intervención. No es prueba de conducción.